


Создано				
Взам. инв. №				
Подл. и дата				
Инв. № подл.				

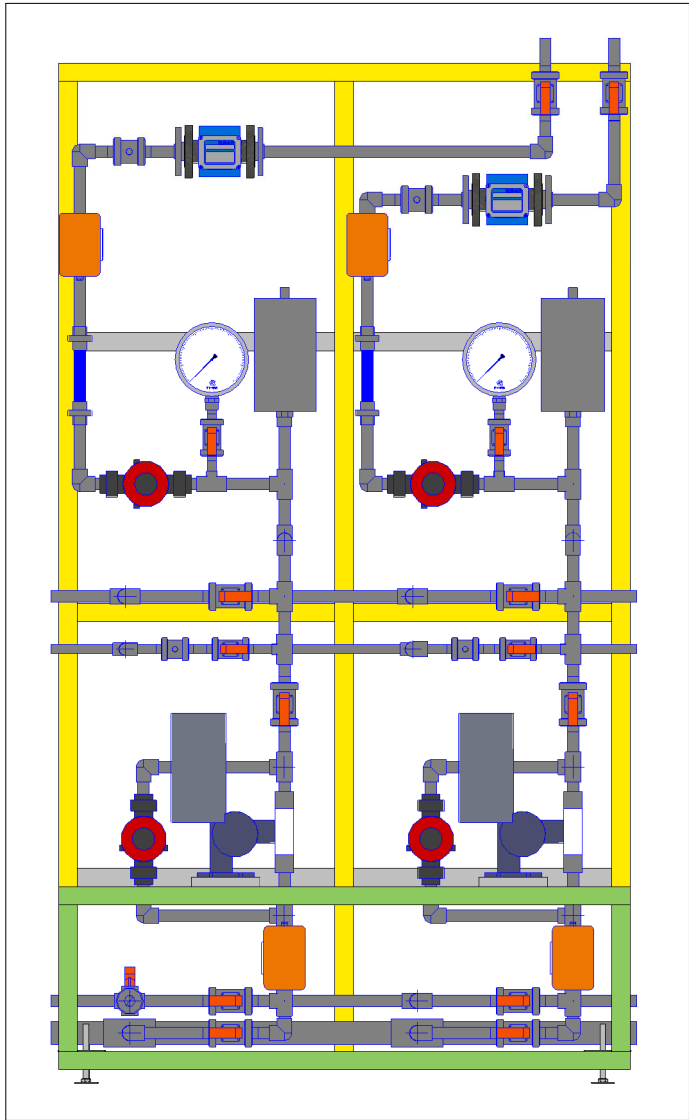

Фасонные части трубопровода

ADSK_Позиция	Наименование	Марка	Завод-изготовитель	Единица измерения	Количество
1.1	Бурт под фланец ПВХ с гладкой поверхностью d=25 мм		COMER	шт.	4
1.2	Двойной адаптер ПВХ (муфтовое/втулочное окончание) с НР 25х32х3/4"	AD12	COMER	шт.	2
1.3	Муфта переходная с ВР 20х1/2"	SO12	COMER	шт.	2
1.4	Переходное кольцо ПВХ 25х20 (Fig. A)	RB90	COMER	шт.	2
1.5	Свободный фланец ПВХ d=25 мм		COMER	шт.	4
1.6	Смотровое стекло ПВХ муфтовое окончания разборное d=25		COMER	шт.	2
1.7	Тройник ПВХ клеевой 90° 20х20		COMER	шт.	2
1.8	Тройник ПВХ клеевой 90° 25х25		COMER	шт.	15
1.9	Тройник переходной ПВХ клеевой 90° 25х20		COMER	шт.	4
1.10	Тройник переходной ПВХ клеевой 90° 50х25		COMER	шт.	2
1.11	Угол клеевой ПВХ 90° d20		COMER	шт.	1
1.12	Угол клеевой ПВХ 90° d25		COMER	шт.	26

Арматура трубопровода

ADSK_Позиция	Наименование	Марка	Завод-изготовитель	Единица измерения	Количество
2.1	Манометр ТМВ серия 21	ТМВ-621Р.00(-0,1-0,3МПа) М20х1,5,1,0	ЗАО "РОСМА"	шт.	2
2.2	Обратный клапан ПВХ муфтовое окончание под клей d20 PN16 FPM	CVD30	COMER	шт.	2
2.3	Обратный клапан ПВХ муфтовое окончание под клей d25 PN16 FPM	CVD30	COMER	шт.	2
2.4	PCM-05.05CM с ПРП-25	PCM-05.05CM с ПРП-25	СООО АРВАС	1 шт.	2
2.5	Шаровый кран BV110 d25 PN16 с муфт. окончанием под клей корпус - PVC-U шар - PVC-U уплотнение - EPDM с электрическим приводом EAQ-MINI-030 - 220 В AC отк./закр. время срабатывания 15 сек.	BV110+EAQ-MINI	COMER	шт.	4
2.6	Шаровый кран муфтовое окончание под клей d20 PN16 EPDM	BV110	COMER	шт.	4
2.7	Шаровый кран муфтовое окончание под клей d25 PN16 EPDM	BV110	COMER	шт.	11

						Номер проекта -				
						Наименование проекта				
Изм.	Кол.уч.	Лист	№ док.	Подп.	Дата	Наименование здания.	Стадия	Лист	Листов	
							РД	003		
							Без имени	Название / логотип		