


Инв. № подл.	Подп. и дата	Взам. инв. №	Согласовано		

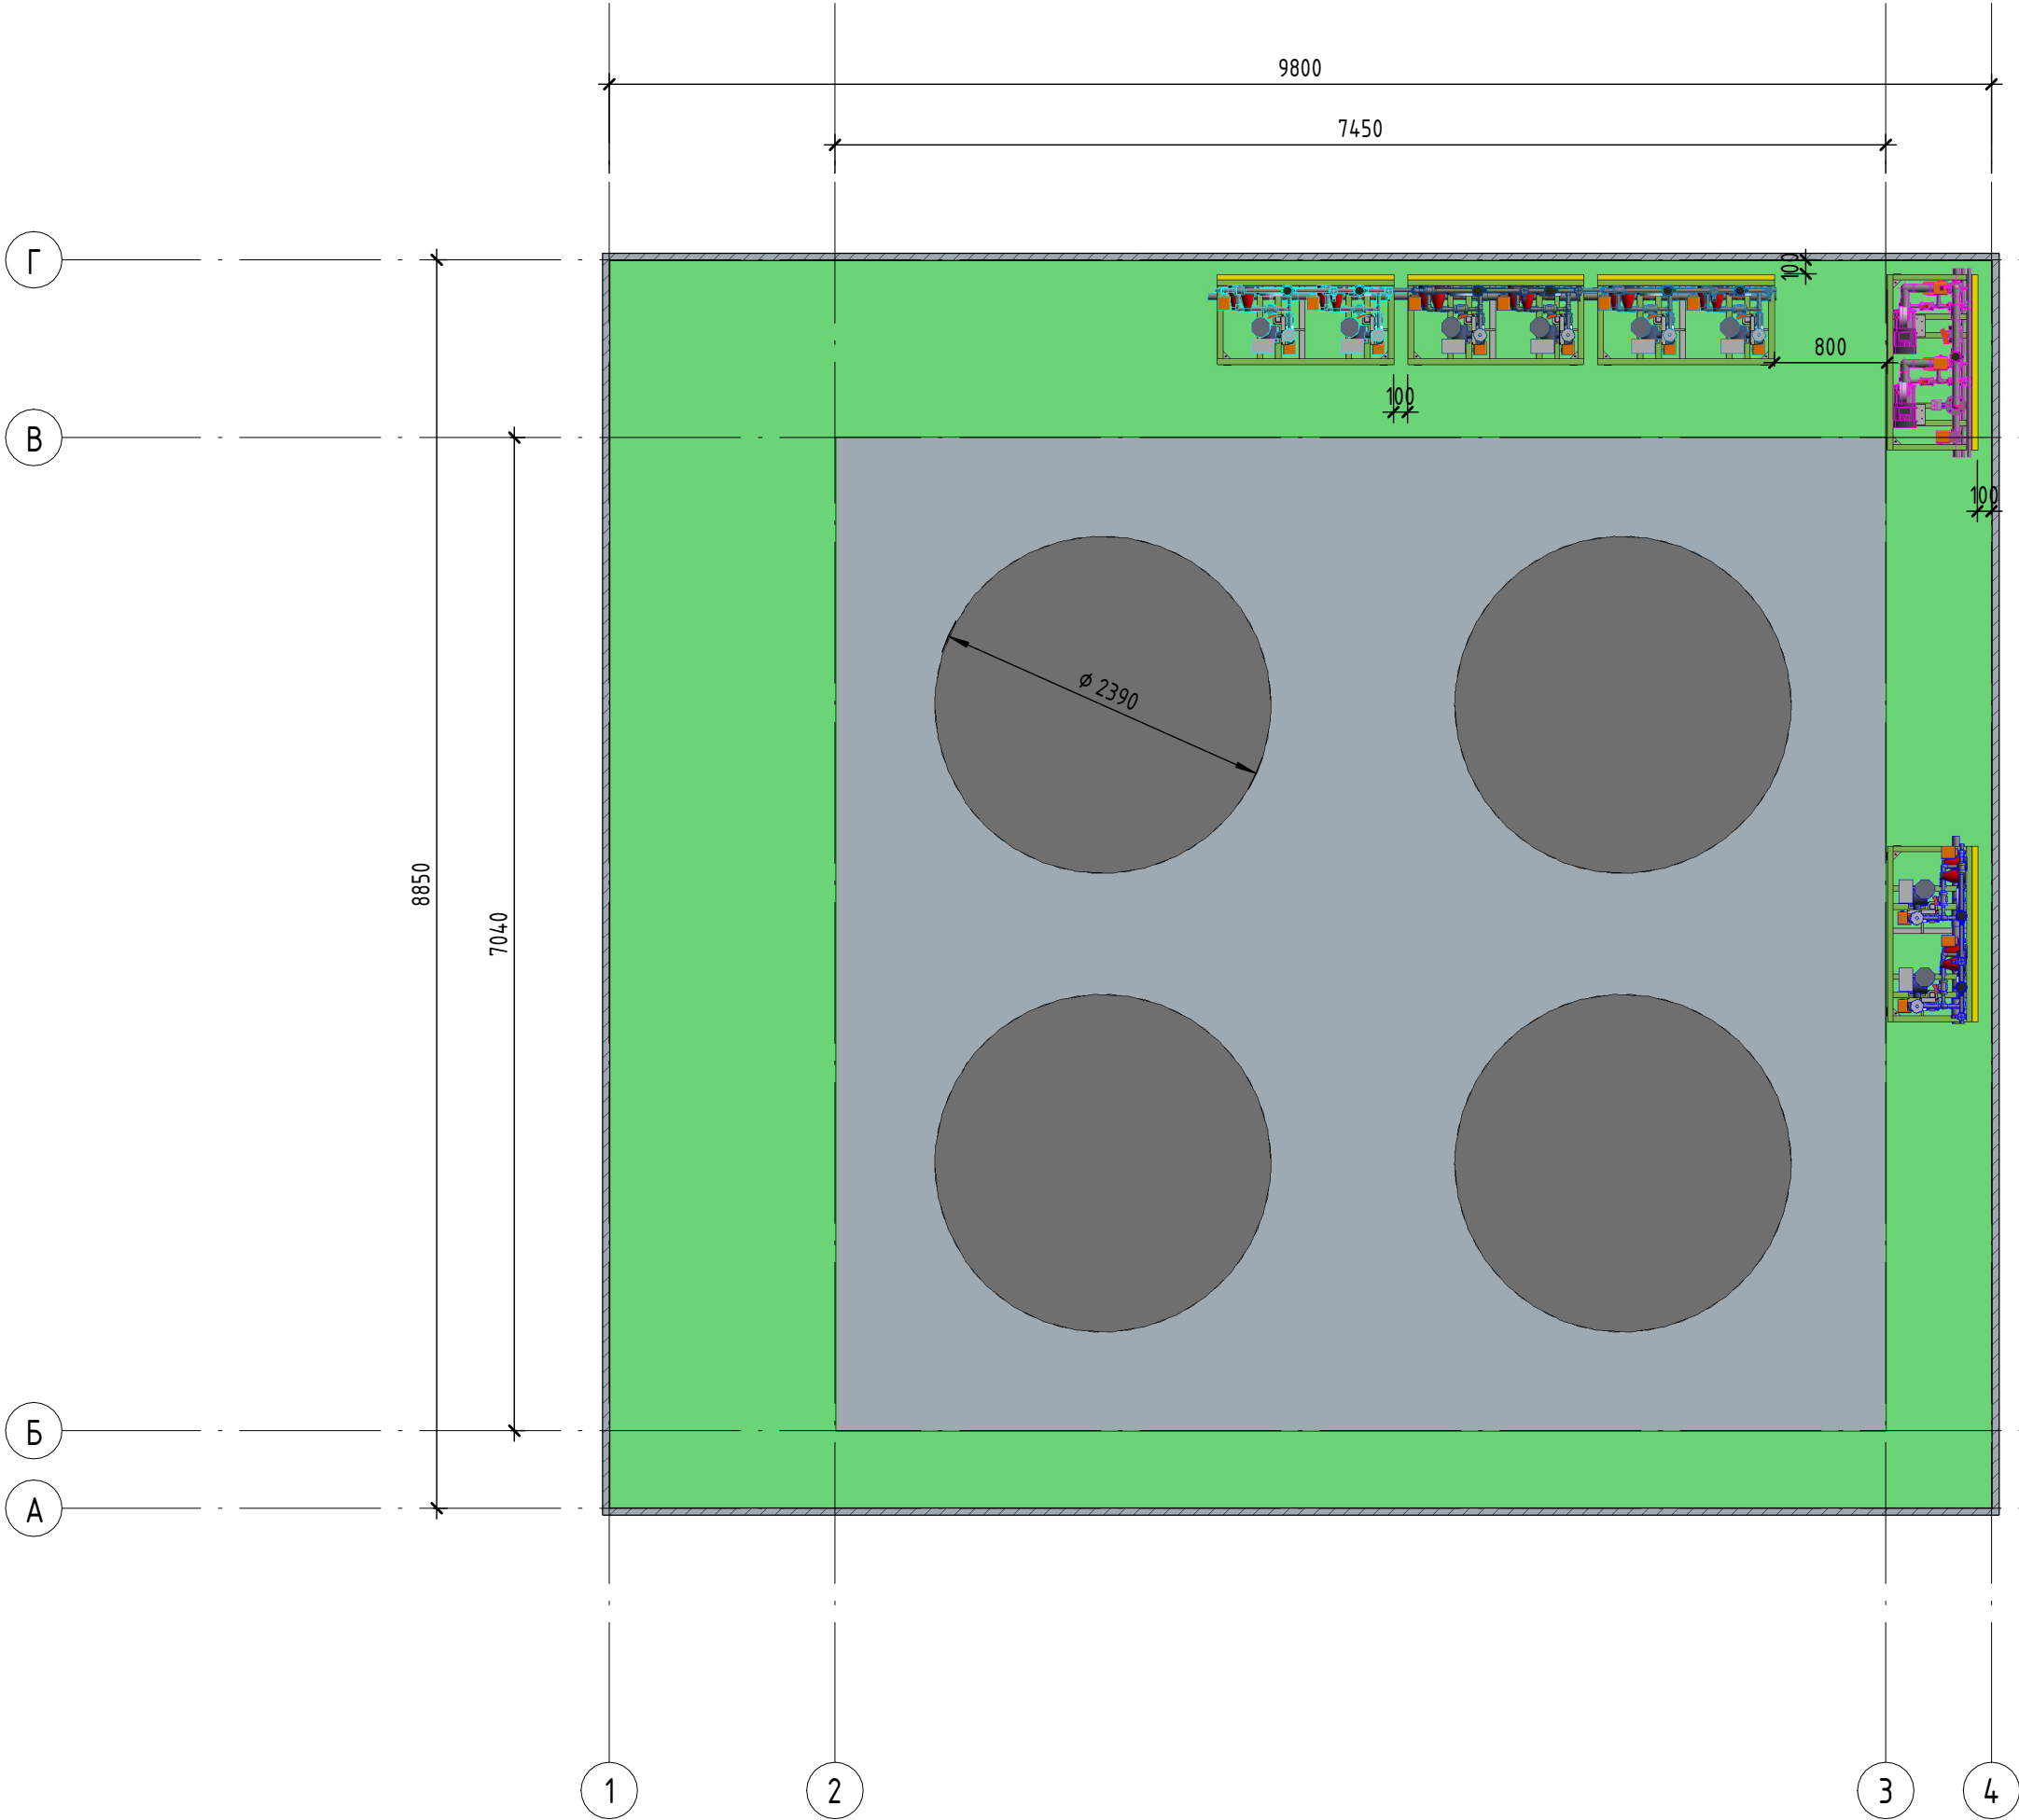

Изм.	Кол.уч.	Лист	№ док.	Подп.	Дата	Номер проекта -	Лист
							007





ADSK_Позиция	Наименование	Марка	Завод-изготовитель	Единица измерения	Количество
1.1	Двойной ниппель ПВХ 3/4"	NI61	COMER	шт.	2
1.2	Муфта переходная с ВР 20х1/2"	S012	COMER	шт.	2
1.3	Муфта разборная переходная ВР 25х3/4"	UN82	COMER	шт.	2
1.4	Переходное кольцо ПВХ 25х20 (Fig. A)	RB90	COMER	шт.	2
1.5	Переходное кольцо резьбовое ПВХ наружная/внутренняя резьба GxG1 1"x3/4"	RB91	COMER	шт.	2
1.6	Смотровое стекло ПВХ муфтовое окончания разборное d=25		COMER	шт.	2
1.7	Тройник 90 ПВХ с внутренней резьбой в центральном патрубке dхG 25х3/4"		COMER	шт.	2
1.8	Тройник ПВХ клеевой 90° 20х20		COMER	шт.	2
1.9	Тройник ПВХ клеевой 90° 25х25		COMER	шт.	14
1.10	Тройник переходной ПВХ клеевой 90° 25х20		COMER	шт.	4
1.11	Тройник переходной ПВХ клеевой 90° 50х25		COMER	шт.	2
1.12	Угол клеевой ПВХ 90° d20		COMER	шт.	1
1.13	Угол клеевой ПВХ 90° d25		COMER	шт.	23

ADSK_Позиция	Наименование	Марка	Завод-изготовитель	Единица измерения	Количество
2.1	Манометр ТМВ серия 21	ТМВ-621Р.00(-0,1-0,3МПа) M20x1,5,1,0	ЗАО "РОСМА"	шт.	2
2.2	Обратный клапан ПВХ муфтовое окончание под клей d20 PN16 FPM	CVD30	COMER	шт.	2
2.3	Обратный клапан ПВХ муфтовое окончание под клей d25 PN16 FPM	CVD30	COMER	шт.	2
2.4	Шаровой кран BV110 d25 PN16 с муфт. окончанием под клей корпус - PVC-U шар - PVC-U уплотнение - EPDM с электрическим приводом EAQ-MINI-030 - 220 В AC отк./закр. время срабатывания 15 сек.	BV110+EAQ-MINI	COMER	шт.	4
2.5	Шаровой кран муфтовое окончание под клей d20 PN16 EPDM	BV110	COMER	шт.	4
2.6	Шаровой кран муфтовое окончание под клей d25 PN16 EPDM	BV110	COMER	шт.	8

ADSK_Позиция	Спецификация/Tup	Диаметр	Длина
3.1	ПВХ трубы Aquademic® напорные PN 16	20 мм	1.48 м
3.2	ПВХ трубы Aquademic® напорные PN 16	25 мм	11.03 м
3.3	ПВХ трубы Aquademic® напорные PN 16	50 мм	1.80 м

						Номер проекта -			
						Наименование проекта			
Изм.	Кол.уч.	Лист	№ док.	Подп.	Дата				
						Наименование здания.	Стадия	Лист	Листов
							РД	003	
						Без имени	Название / логотип		

Инв. № подл.	Подп. и дата	Взам. инв. №	Согласовано		

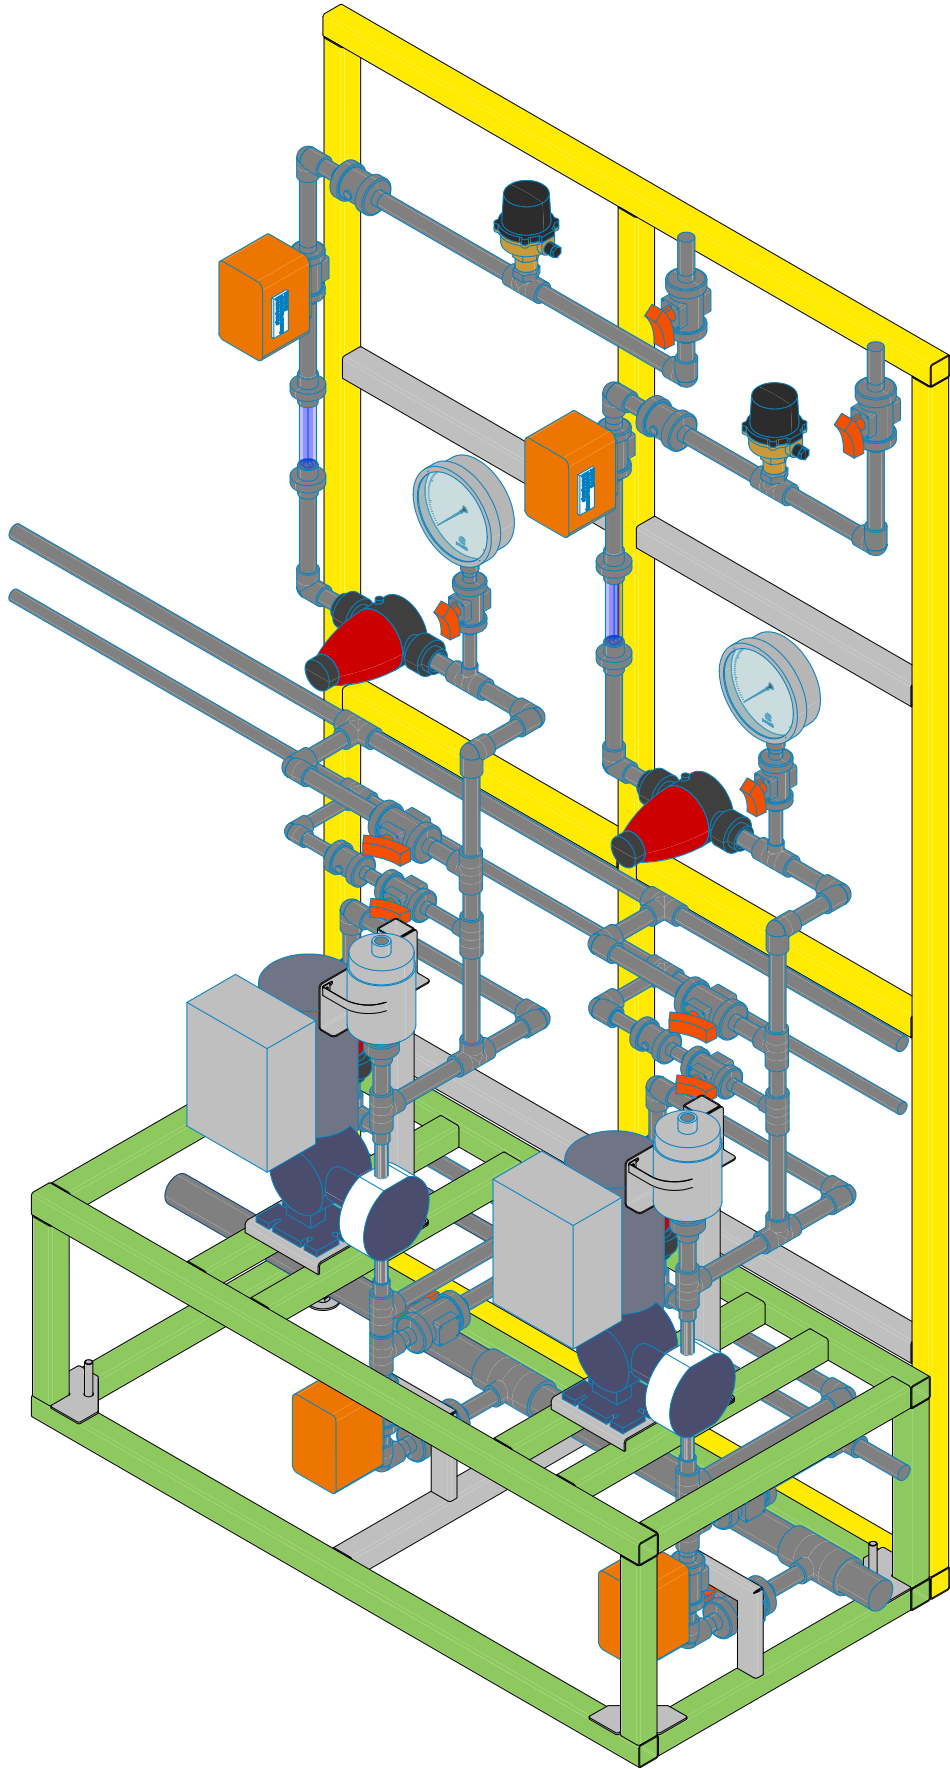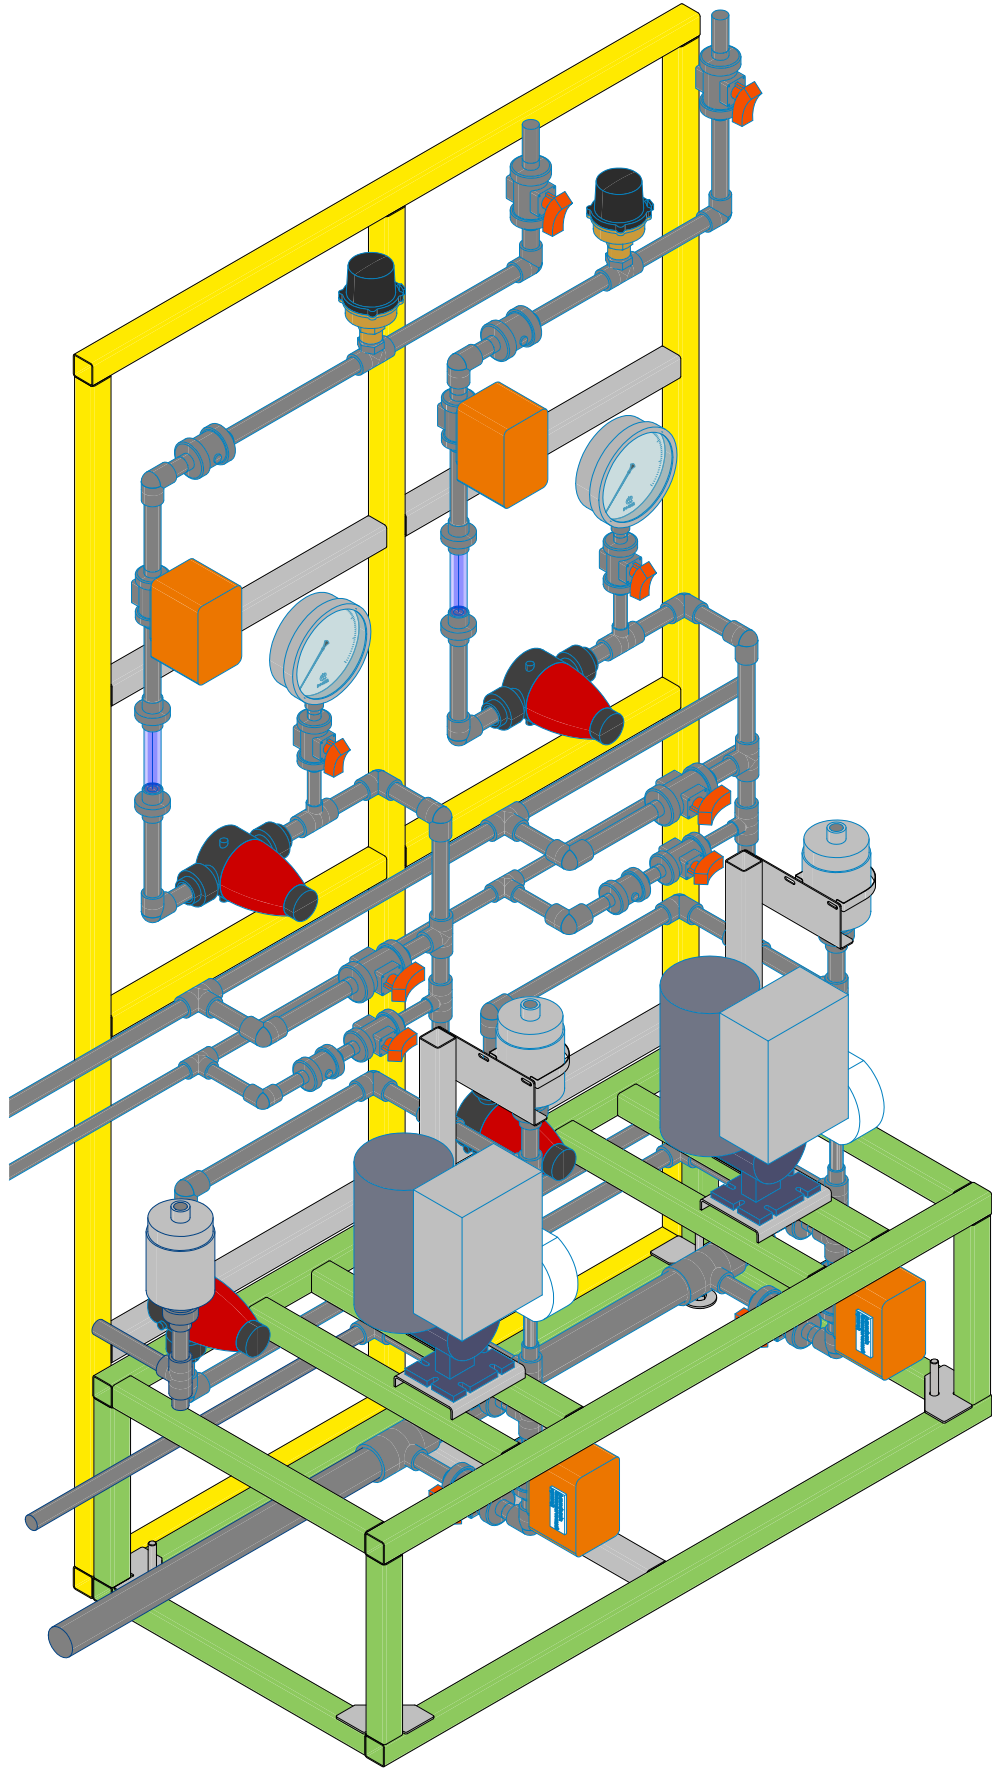

						Номер проекта -	Лист
Изм.	Кол.уч.	Лист	№ док.	Подп.	Дата		004





ADSK_Позиция	Спецификация/Тип	Диаметр	Длина
3.1	ПВХ трубы Aquademic® напорные PN 16	20 мм	2.28 м
3.2	ПВХ трубы Aquademic® напорные PN 16	25 мм	4.16 м
3.3	ПВХ трубы Aquademic® напорные PN 16	50 мм	6.45 м
3.4	ПВХ трубы Aquademic® напорные PN 16	90 мм	1.12 м

ADSK_Позиция	Наименование	Марка	Завод-изготовитель	Единица измерения	Количество
1.1	!!!Переходное кольцо не найдено	RB90	COMER	шт.	2
1.2	Бурт под фланец ПВХ с гладкой поверхностью d=50 мм		COMER	шт.	2
1.3	Муфта переходная с ВР 20х1/2"	S012	COMER	шт.	2
1.4	Муфта разборная переходная НР 50х1 1/2"	US82	COMER	шт.	4
1.5	Переходное кольцо ПВХ 50х25 (Fig. B)	RB90	COMER	шт.	3
1.6	Переходное кольцо ПВХ 90х50 (Fig. B)	RB90	COMER	шт.	6
1.7	Тройник 90 ПВХ с внутренней резьбой в центральном патрубке dхG 50х1"1/2		COMER	шт.	1
1.8	Тройник ПВХ клеевой 90° 20х20		COMER	шт.	2
1.9	Тройник ПВХ клеевой 90° 25х25		COMER	шт.	4
1.10	Тройник ПВХ клеевой 90° 50х50		COMER	шт.	6
1.11	Тройник переходной ПВХ клеевой 90° 50х20		COMER	шт.	4
1.12	Тройник переходной ПВХ клеевой 90° 50х25		COMER	шт.	4
1.13	Угол клеевой ПВХ 90° d20		COMER	шт.	4
1.14	Угол клеевой ПВХ 90° d25		COMER	шт.	4
1.15	Угол клеевой ПВХ 90° d50		COMER	шт.	13

ADSK_Позиция	Наименование	Марка	Завод-изготовитель	Единица измерения	Количество
2.1	Манометр TMB серия 21	TMB-621P.00(-0,1-0,3МПа)M20x1,5,1,0	ЗАО "РОСМА"	шт.	2
2.2	Обратный клапан ПВХ муфтовое окончание под клей d20 PN16 FPM	CVD30	COMER	шт.	2
2.3	Обратный клапан ПВХ муфтовое окончание под клей d25 PN16 FPM	CVD30	COMER	шт.	1
2.4	Обратный клапан ПВХ муфтовое окончание под клей d50 PN16 FPM	CVD30	COMER	шт.	2
2.5	PCM-05.05CM с ПРП-40	PCM-05.05CM с ПРП-40	ООО АРВАС	1 шт.	1
2.6	Шаровой кран BV110 d25 PN16 с муфт. окончанием под клей корпус - PVC-U шар - PVC-U уплотнение - EPDM с электрическим приводом EAQ-MINI-030 - 220 В АС отк./закр. время срабатывания 15 сек.	BV110+EAQ-MINI	COMER	шт.	1
2.7	Шаровой кран BV110 d50 PN16 с муфт. окончанием под клей корпус - PVC-U шар - PVC-U уплотнение - EPDM с электрическим приводом EAQ-MINI-030 - 220 В АС отк./закр. время срабатывания 15 сек.	BV110+EAQ-MINI	COMER	шт.	4
2.8	Шаровой кран муфтовое окончание под клей d20 PN16 EPDM	BV110	COMER	шт.	6
2.9	Шаровой кран муфтовое окончание под клей d25 PN16 EPDM	BV110	COMER	шт.	4
2.10	Шаровой кран муфтовое окончание под клей d50 PN16 EPDM	BV110	COMER	шт.	2

						Номер проекта -			
						Наименование проекта			
Изм.	Кол.уч.	Лист	№ док.	Подп.	Дата				
						Наименование здания.	Стадия	Лист	Листов
							РД	005	
						Без имени	Название / логотип		

Инв. № подл.	Подп. и дата	Взам. инв. №	Согласовано		

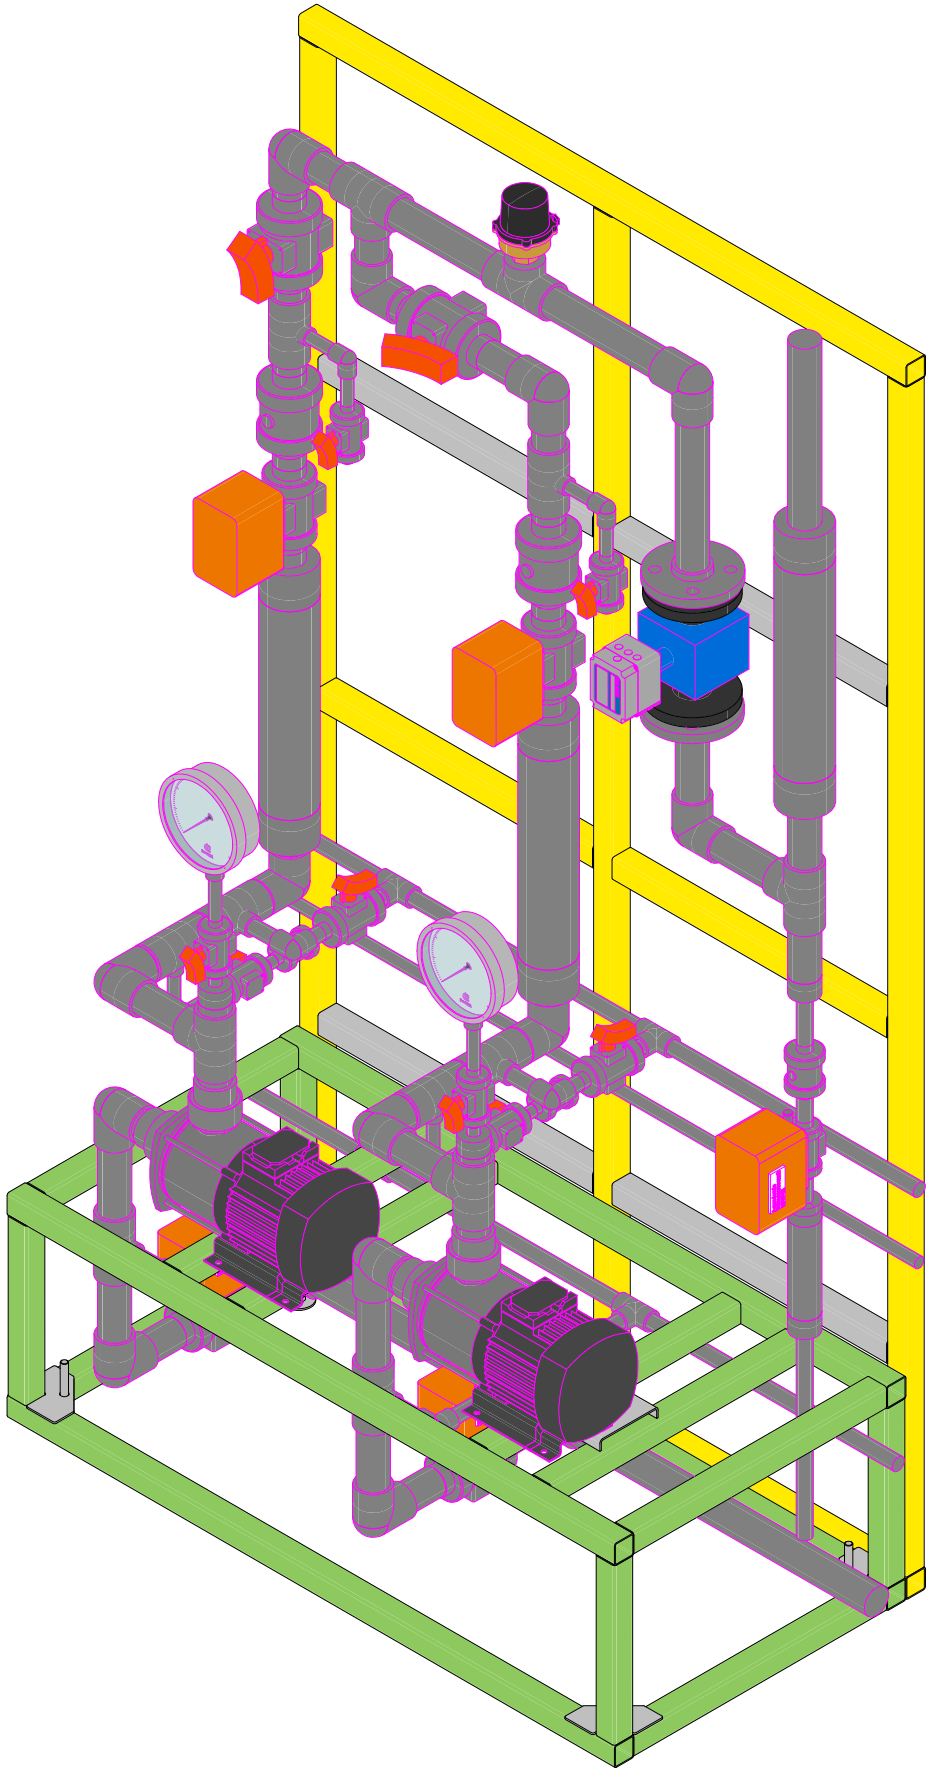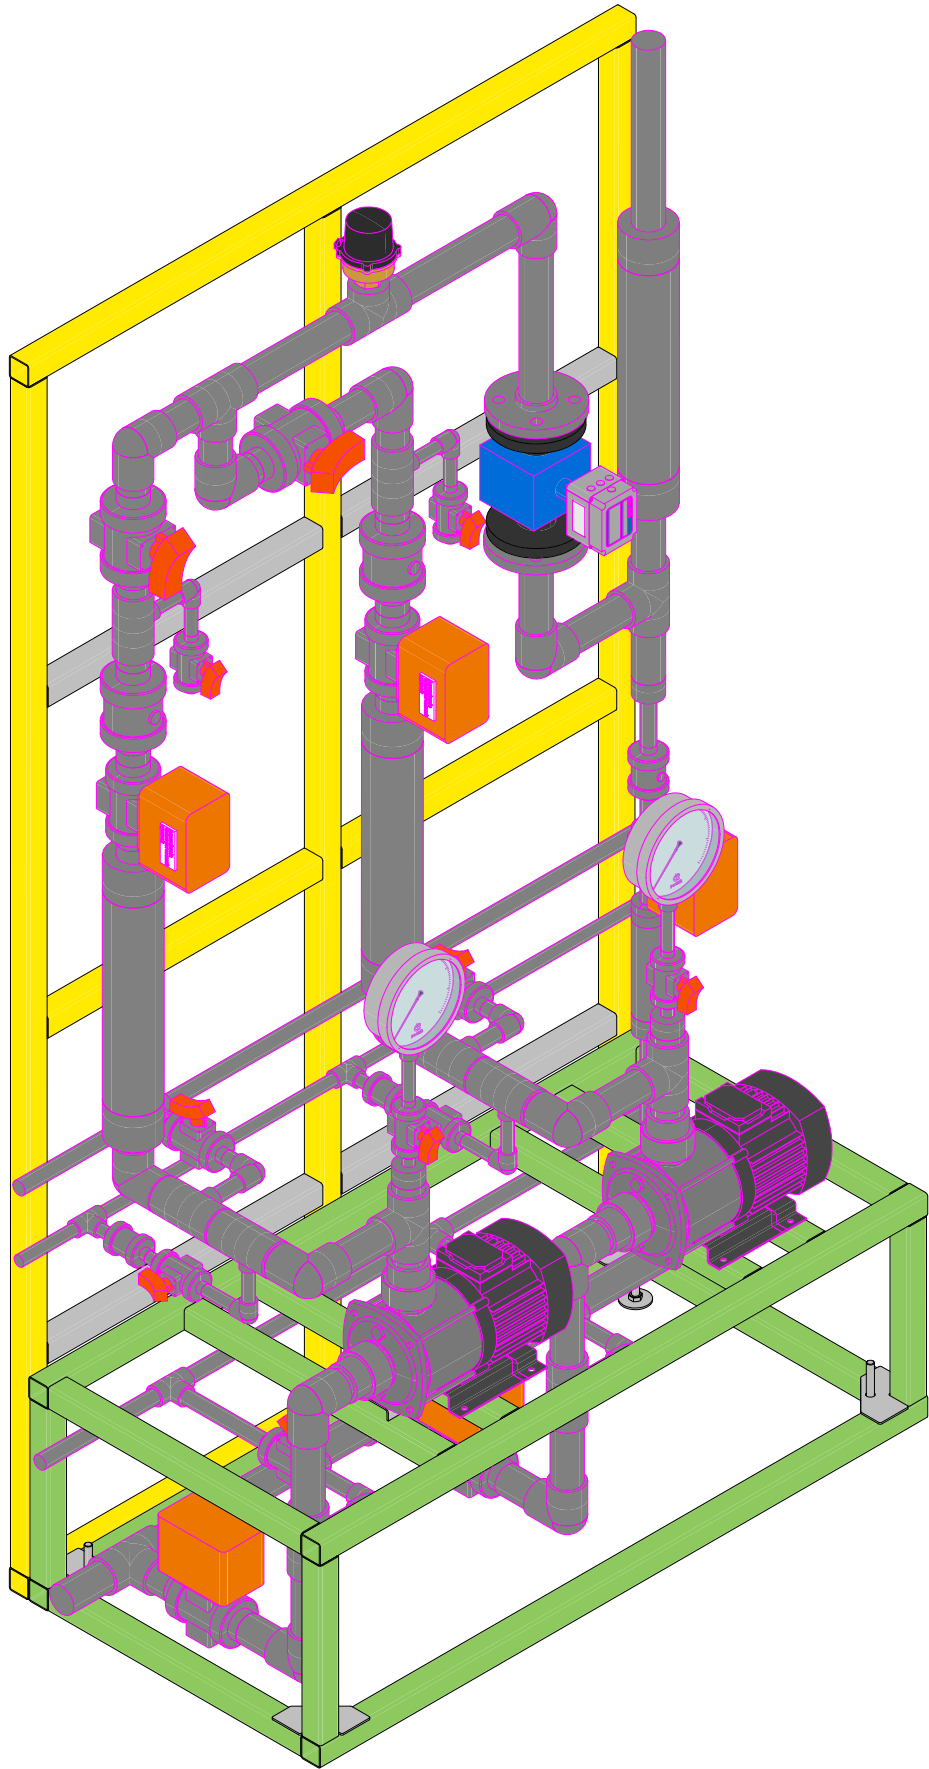

						Номер проекта -	Лист
Изм.	Кол.уч.	Лист	№ док.	Подп.	Дата		006