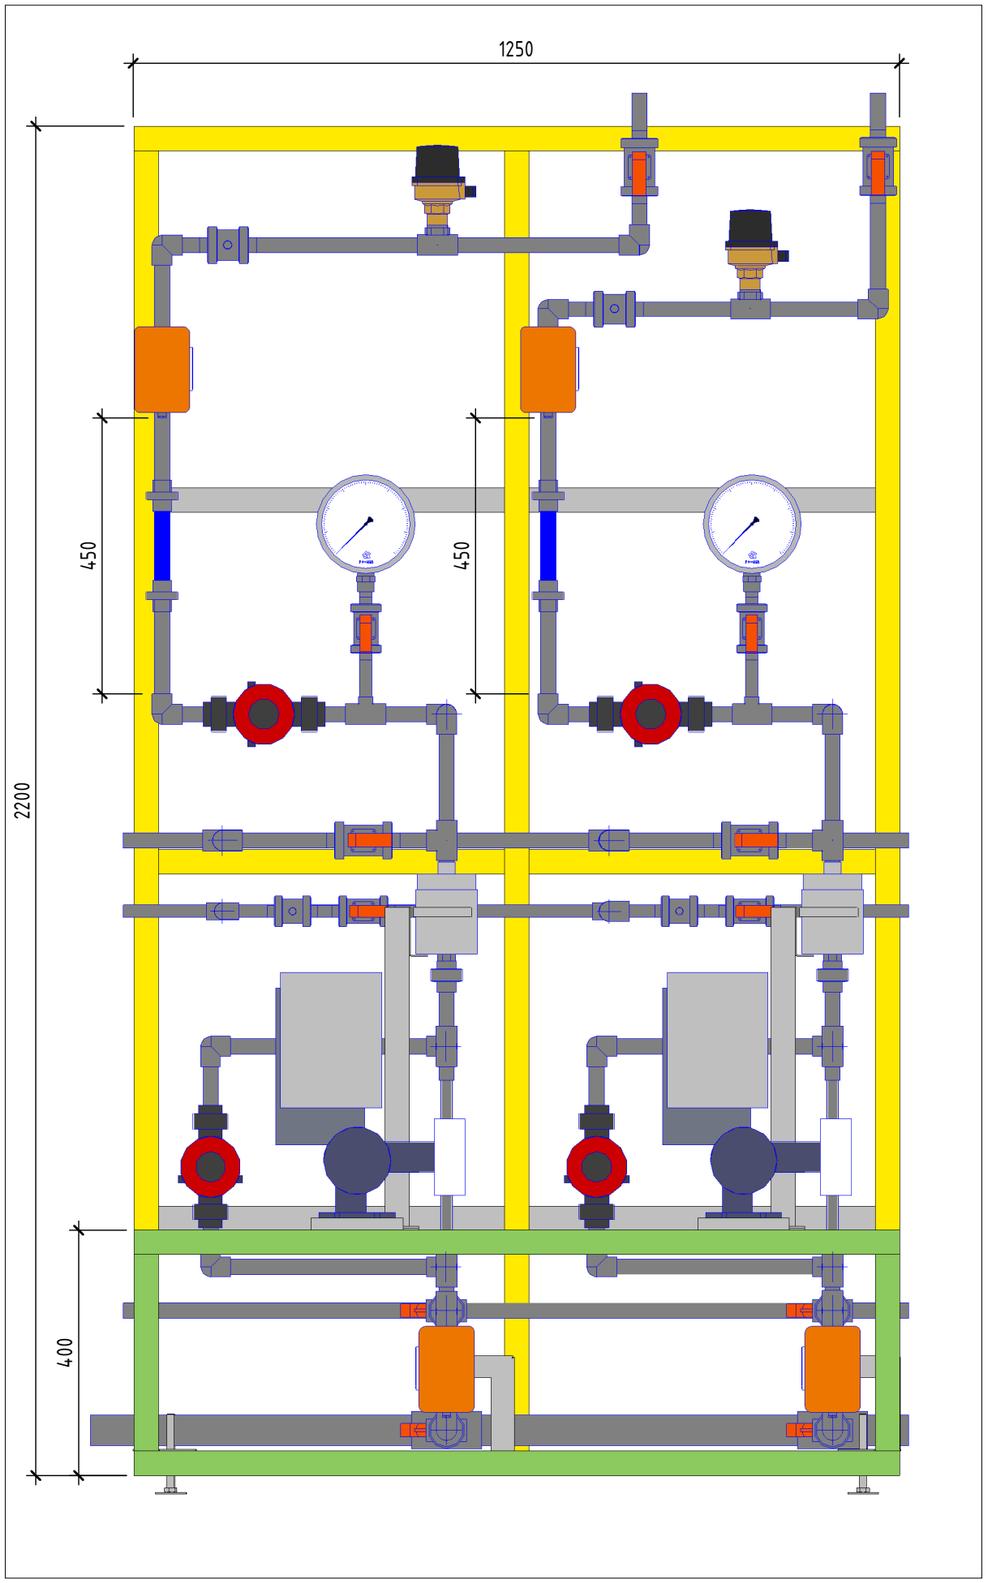

Фасонные части трубопровода

ADSK_Позиция	Наименование	Марка	Завод-изготовитель	Единица измерения	Количество
1.1	Двойной ниппель ПВХ 3/4''	NI61	COMER	шт.	2
1.2	Муфта переходная с ВР 20x1/2''	SO12	COMER	шт.	2
1.3	Муфта разборная переходная ВР 25x3/4''	UN82	COMER	шт.	2
1.4	Переходное кольцо ПВХ 25x20 (Fig. A)	RB90	COMER	шт.	2
1.5	Переходное кольцо резьбовое ПВХ наружная/ внутренняя резьба GxG1 1''x3/4''	RB91	COMER	шт.	2
1.6	Смотровое стекло ПВХ муфтовое окончания разборное d=25		COMER	шт.	2
1.7	Тройник 90 ПВХ с внутренней резьбой в центральном патрубке dxG 25x3/4''		COMER	шт.	2
1.8	Тройник ПВХ клеевой 90° 20x20		COMER	шт.	2
1.9	Тройник ПВХ клеевой 90° 25x25		COMER	шт.	14
1.10	Тройник переходной ПВХ клеевой 90° 25x20		COMER	шт.	4
1.11	Тройник переходной ПВХ клеевой 90° 50x25		COMER	шт.	2
1.12	Угол клеевой ПВХ 90° d20		COMER	шт.	1
1.13	Угол клеевой ПВХ 90° d25		COMER	шт.	23

Арматура трубопровода

ADSK_Позиция	Наименование	Марка	Завод-изготовитель	Единица измерения	Количество
2.1	Манометр ТМВ серия 21	ТМВ-621Р.00(-0,1-0,3МРа) М20x1,5.1,0	ЗАО "РОСМА"	шт.	2
2.2	Обратный клапан ПВХ муфтовое окончание под клей d20 PN16 FPM	CVD30	COMER	шт.	2
2.3	Обратный клапан ПВХ муфтовое окончание под клей d25 PN16 FPM	CVD30	COMER	шт.	2
2.4	Шаровой кран BVI10 d25 PN16 с муфт. окончанием под клей корпус - PVC-U шар - PVC-U уплотнение - EPDM с электрическим приводом EAQ-MINI-030 - 220 В АС отк./закр. время срабатывания 15 сек.	BVI10+EAQ-MINI	COMER	шт.	4
2.5	Шаровой кран муфтовое окончание под клей d20 PN16 EPDM	BVI10	COMER	шт.	4
2.6	Шаровой кран муфтовое окончание под клей d25 PN16 EPDM	BVI10	COMER	шт.	8

Трубопроводы

ADSK_Позиция	Спецификация/Тип	Диаметр	Длина
3.1	ПВХ трубы Aquademic® напорные PN 16	20 мм	1.96 м
3.2	ПВХ трубы Aquademic® напорные PN 16	25 мм	10.71 м
3.3	ПВХ трубы Aquademic® напорные PN 16	50 мм	1.23 м

Согласовано

Взам. инв. №

Подп. и дата

Инв. № подл.

Изм.	Кол.уч.	Лист	№док.	Подп.	Дата

Номер проекта -

Наименование проекта

Наименование здания.	Стадия	Лист	Листов
	РД	003	

Без имени

Название / логотип

Формат А3А